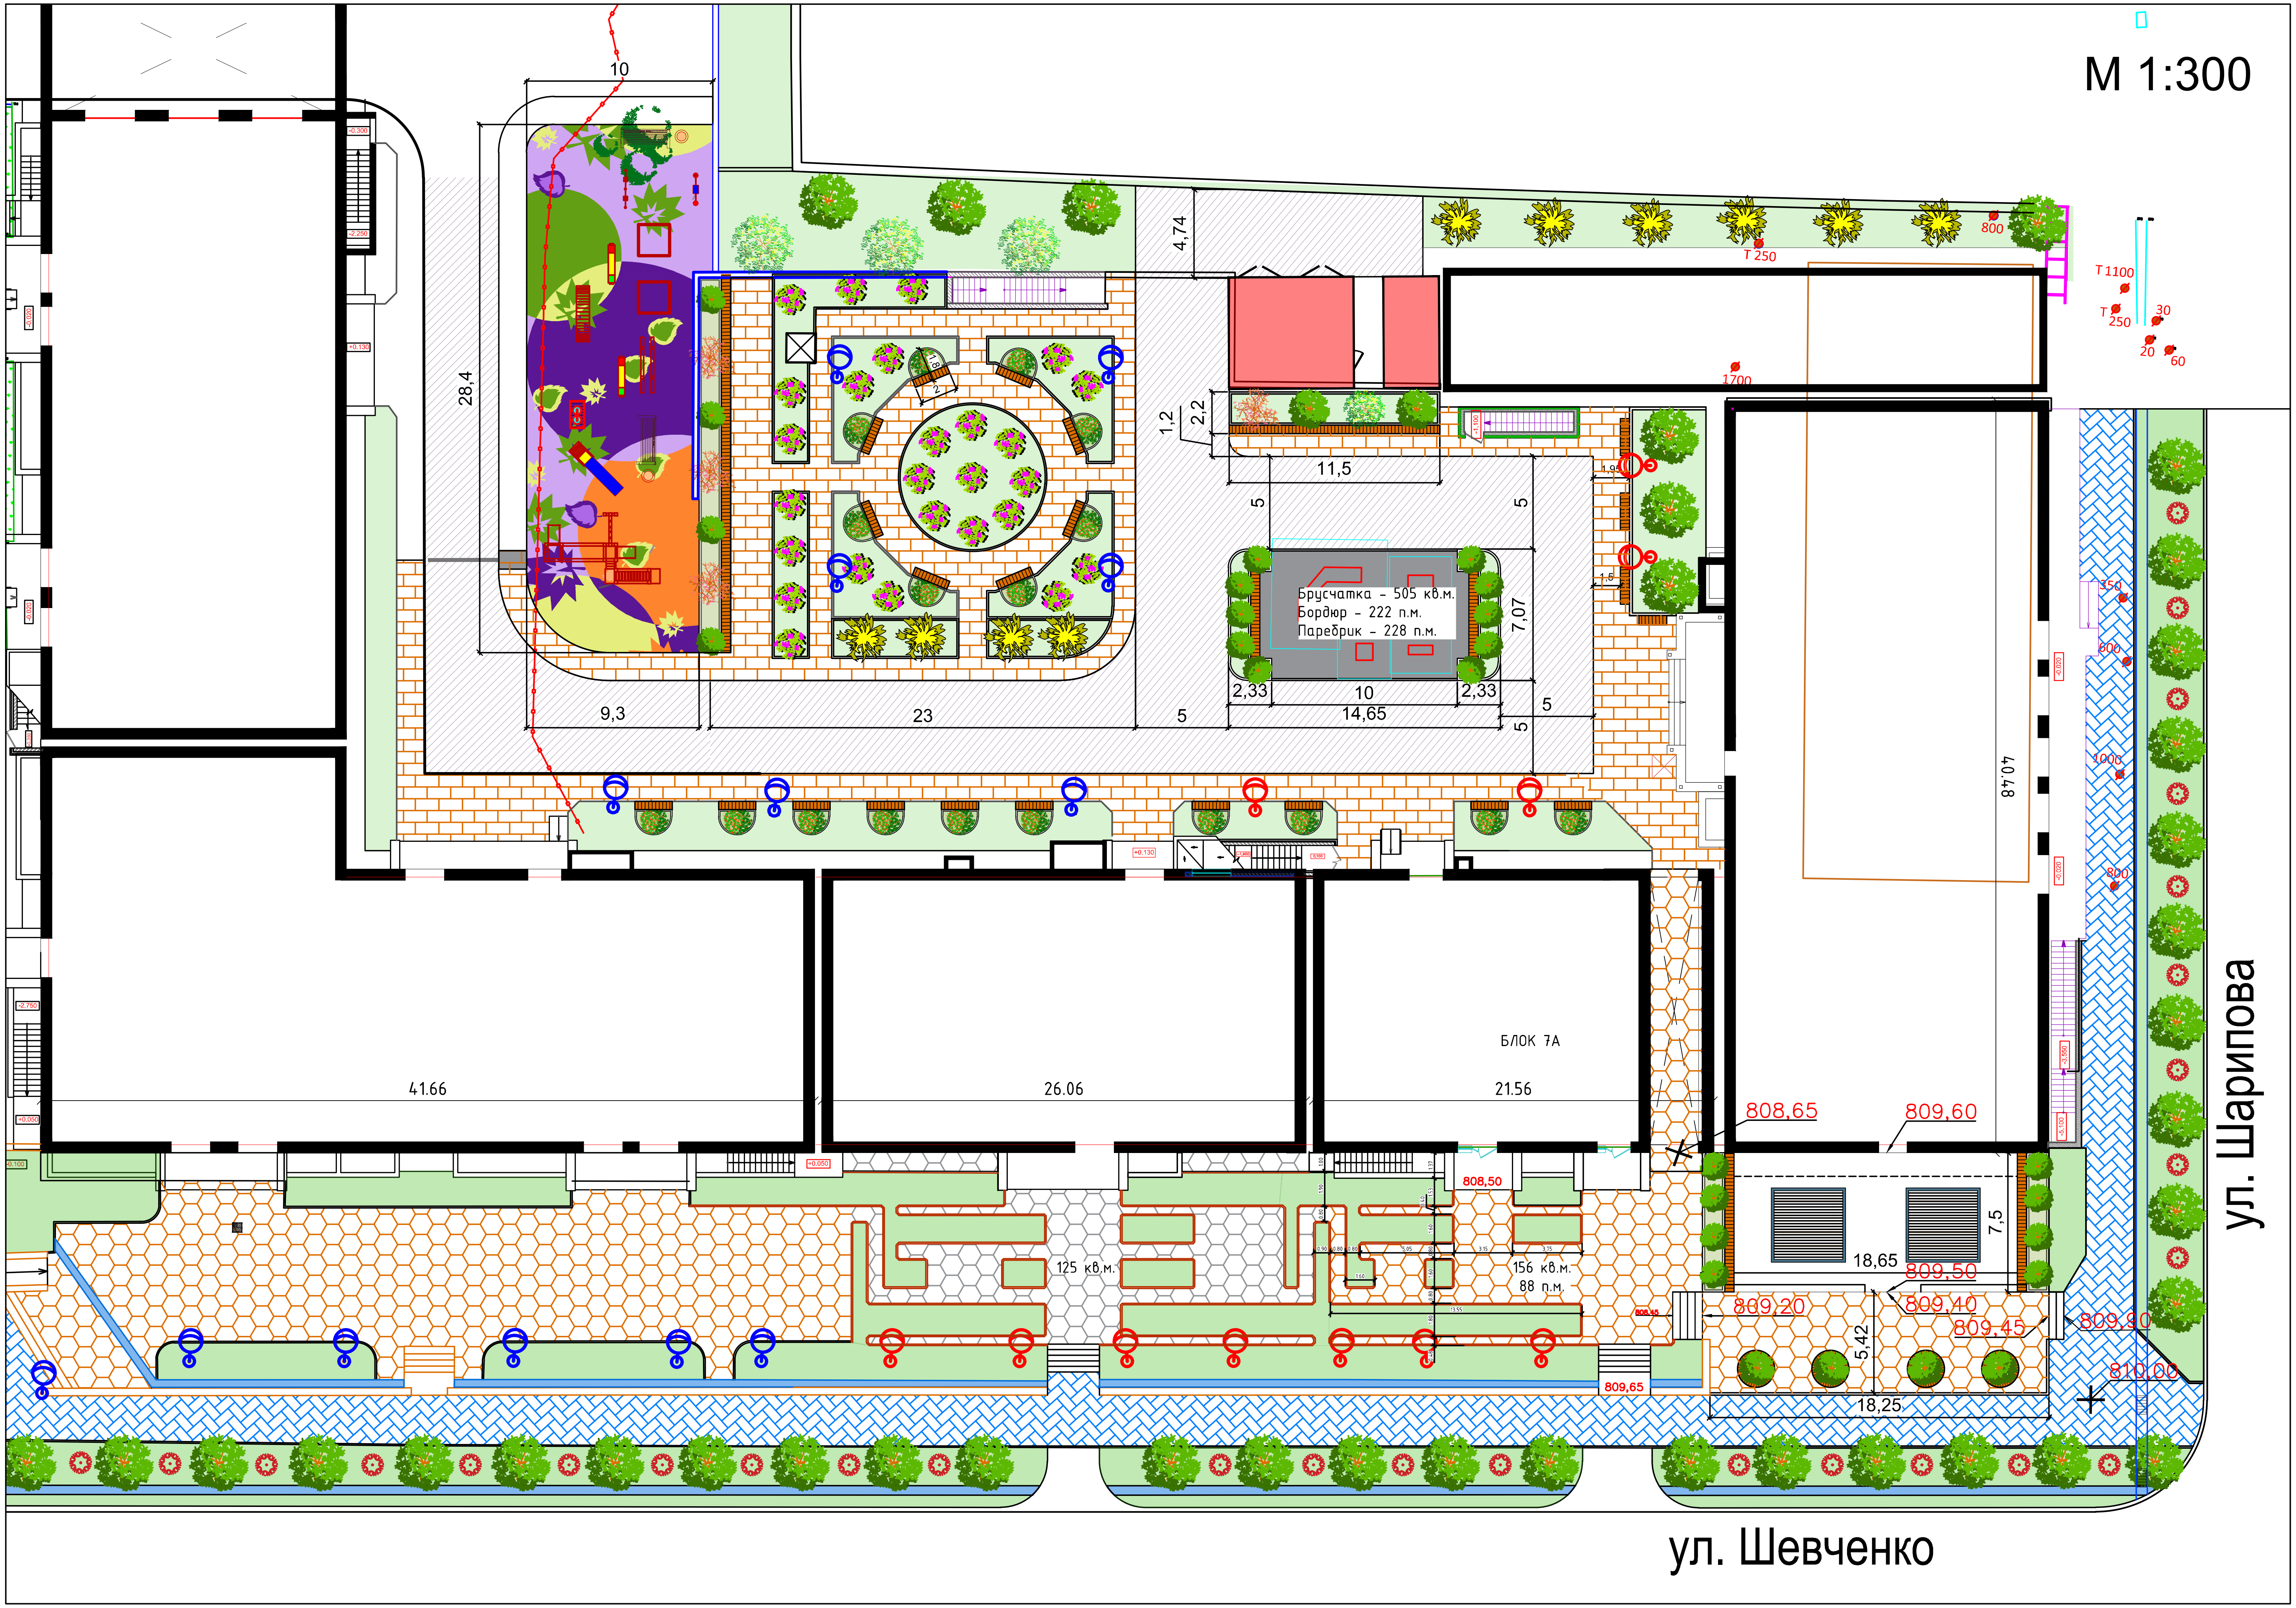
М 1:300
10
28,4
4,74
1,2
2,2
11,5
5
5
Брусчатка – 505 кв.м.
Бордюр – 222 п.м.
Парeбрик – 228 п.м.
7,07
2,33
10
2,33
14,65
9,3
23
5
5
5
Т 250
800
Т 1100
Т 250
30
20
60
1700
350
600
1000
800
40.48
41.66
26.06
БЛОК 7А
21.56
808,65
809,60
808,50
125 кв.м.
156 кв.м.
88 п.м.
7,5
18,65
809,50
809,20
809,40
809,45
809,90
5,42
810,00
18,25
809,65
ул. Шарипова
ул. Шевченко